



+

darin dach

design

The Commons

540 Lakes Street

Excelsior, MN 55331

PH: (612) 701-7117



EST. 2019

CHANHASSEN

BREWING COMPANY

I HEREBY CERTIFY THAT THIS PLAN, SPECIFICATION, OR REPORT WAS PREPARED BY ME OR UNDER MY DIRECT SUPERVISION AND THAT I AM A LICENSED PROFESSIONAL ENGINEER IN THE STATE OF MINNESOTA



Tommy C. Maynard

MEP EIT

JUNE 26, 2022

PROJECT TITLE:

CHANHASSEN BREWING

951 West 78th Street

Chanhassen, MN 55317

CUMULATIVE REVISIONS:

MARK	DATE	DESCRIPTION
-	11/4/2020	2020 PERM SET
△	10/4/2020	PERM SET
△	10/30/2020	PERM SET
△	10/30/2020	PERM SET
△	12/4/2020	REVISION SET

PROJECT #:

2020-020

DRAWN BY:

T


CHECK BY:

T

© 2019 MAGNEY ARCHITECTURE

PROPOSED FLOOR PLAN

A201

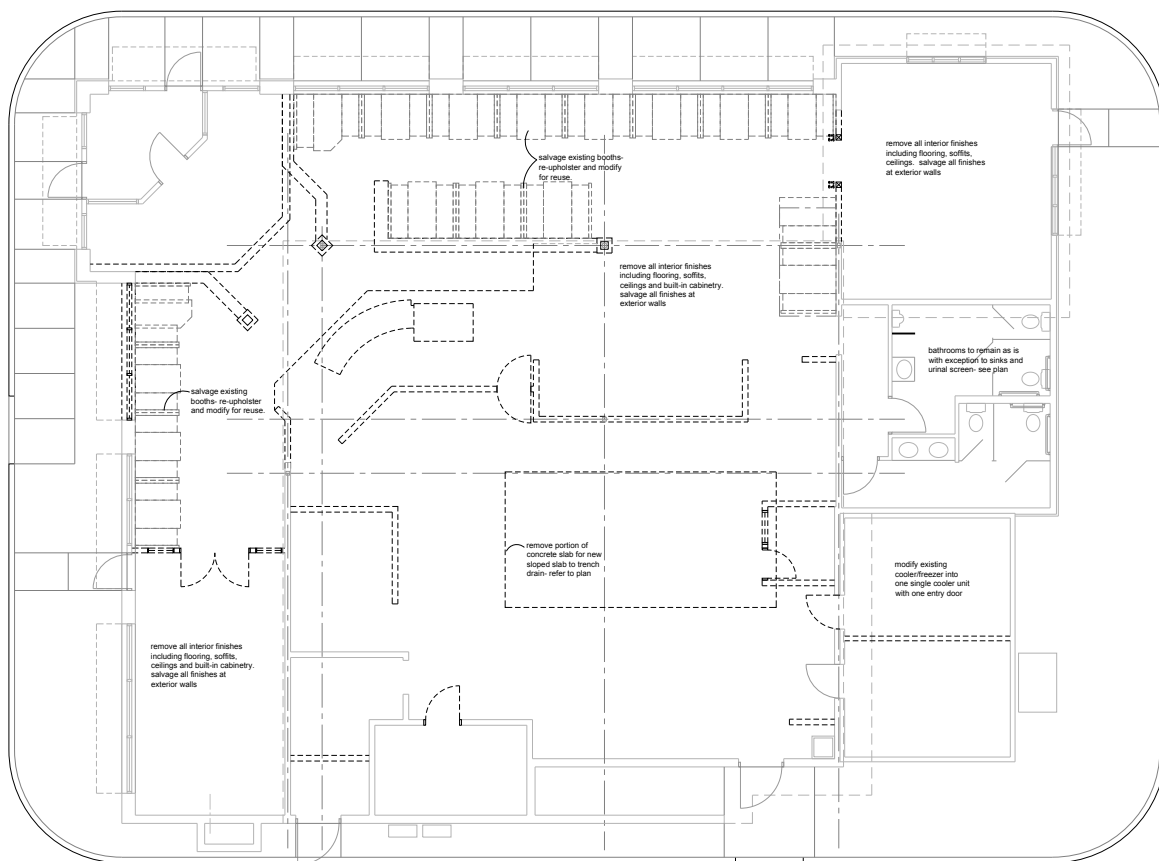

remove all interior finishes
including flooring, soffits,
ceilings. salvage all finishes
at exterior walls

remove all interior finishes including flooring, soffits, ceilings and built-in cabinetry. salvage all finishes at exterior walls

- salvage existing booths- re-upholster and modify for reuse.

remove all interior finishes including flooring, soffits, ceilings and built-in cabinetry. salvage all finishes at exterior walls

remove portion of concrete slab for new sloped slab to trench drain- refer to plan

modify existing
cooler/freezer into
one single cooler unit
with one entry door


DEMOLITION (EXISTING) PLAN
1/4" = 1'-0"

1 NORTH ELEVATION
1/4" = 1'-0"


WEST ELEVATION
1/4" = 1'-0"

A401

FOR CONSTRUCTION - REVISED 12/14/2020

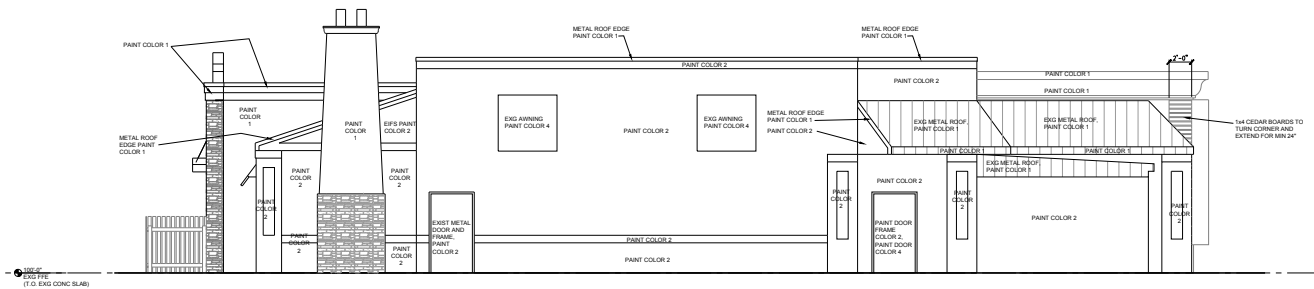

SOUTH ELEVATION
1/4" = 1'-0"

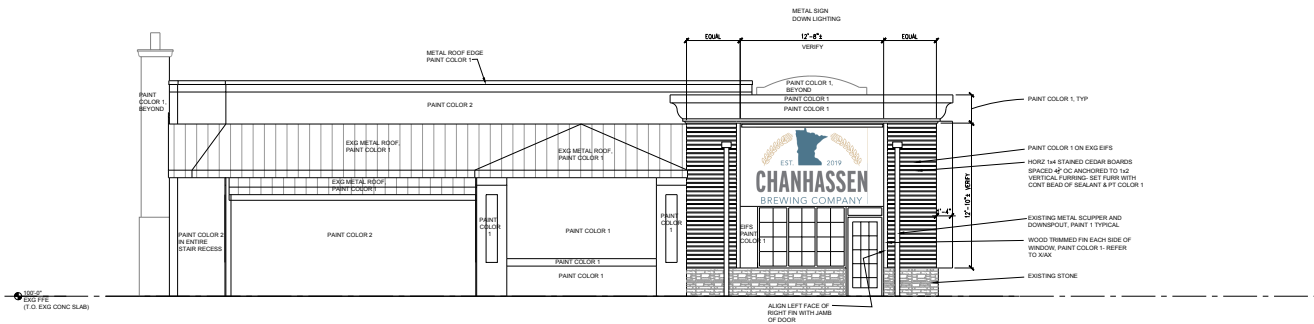

EAST ELEVATION
1/4" = 1'-0"

MAGNEY
ARCHITECTURE

+ darin duch
design

The Commons
540 Lake Street
Excelsior, MN 55331
PH: (612) 701-7117

EST. 1979
CHANHASSEN
BREWING COMPANY

1. VERIFY EXISTING 1/4" METAL ROOF
SPECIFICATION, OR VERIFY WITH
PROVIDER OF EX. OR VERIFY WITH
SPECIFICATION. THE 1/4" IS A BELL
LOCATED INSIDE THE 1/4" OF
EX. SIDE OF ROOF.

Tammy S. Magney
LICENSE NUMBER
19917 JUNE 30, 2022

PROJECT TITLE:

CHANHASSEN
BREWING
951 West 78th Street
Chanhassen, MN 55317

SUBMITTAL REVISIONS:

REVISION	DATE	DESCRIPTION
1	11/16/2020	EXG FRAME SET
2	11/24/2020	EXG FRAME SET
3	12/01/2020	EXG FRAME SET
4	12/08/2020	EXG FRAME SET
5	12/14/2020	EXG FRAME SET

PROJECT # 2020-0201
DRAWN BY: [Signature]
CHECK BY: [Signature]
© 2021 Magney Architecture


EXTERIOR ELEVATIONS

FOR CONSTRUCTION - REVISED 12/14/2020

A402



MAGNEY	
ARCHITECTURE	
+ darin duchs	
design	
The Commons 540 Lake Street Excelsior, MN 55331 PH: (612) 701-7117	
	
CHANHASSEN BREWING COMPANY	
I HEREBY CERTIFY that this plan, SPECIFICATION, OR REPORT WAS PREPARED BY ME OR UNDER MY DIRECT SUPERVISION AND THAT I AM A duly LICENSED PROFESSIONAL ENGINEER IN THE STATE OF MINNESOTA. <i>Darín Duchs</i> Tammy S. Mauney LICENSE NUMBER: 18017 APR 26, 2022	
PROJECT TITLE:	
CHANHASSEN BREWING 951 West 78th Street Chanhassen, MN 55317	
CLIMATICAL REVISIONS:	
MARK	DATE DESCRIPTION
(A)	11/16/2020 DEWD PERM SET
(B)	11/24/2020 PERM SET
(C)	32/10/2020 PERM SET
(D)	12/14/2020 PERM SET
(E)	12/14/2020 REVISION SET
PROJECT #:	
DRAWN BY:	
CHECK BY:	
© 2011 Wipac Industries	
BAR ENLARGED PLAN, WALL SECTIONS A501	

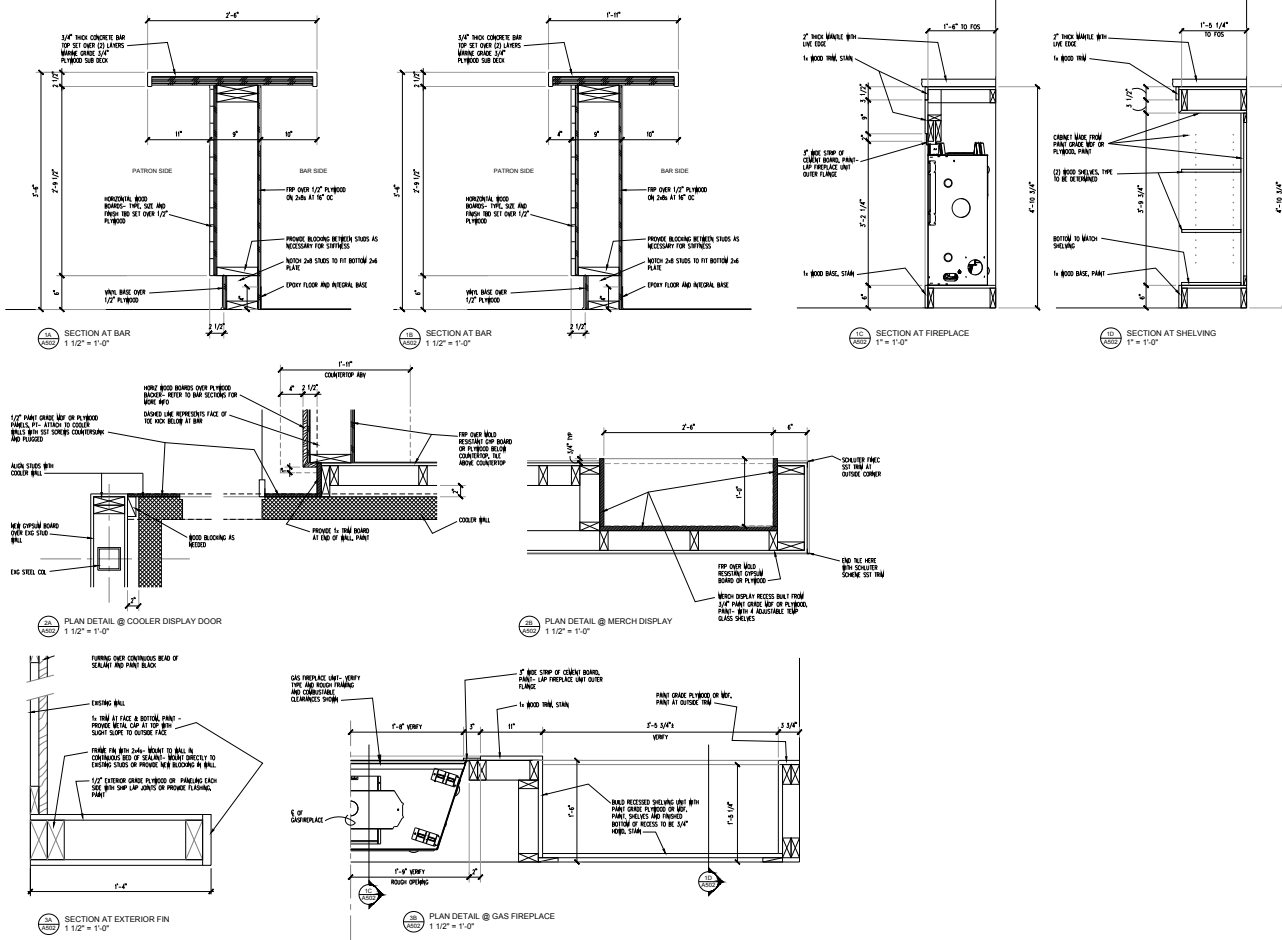

MAGNEY
ARCHITECTURE

darin duch
d e s i g n

The Commons
540 Lake Street
Excelsior, MN 55331
PH: (612) 701-7117

LET US
CHANHASEN
BREWING COMPANY

1. VERIFY EXISTING 3401 THIS BUILDING SPECIFICATION, OR REPORT WITH PERMITS OR AS OF ANY APPLICABLE SPECIFICATION, THE TYPE OF A BUILDING LOCATED INSIDE THE CITY OF THE STATE OF MINNESOTA.

James S. Magney

Tammy S. Magney
LICENSE NUMBER
19917 JUNE 30, 2022

PROJECT TITLE

CHANHASEN
BREWING
951 West 78th Street
Chanhassen, MN 55317

SUBMITTAL/REVISIONS:


REVISION	DATE	DESCRIPTION
1	11/16/2020	ISSUE PERMIT SET
2	11/24/2020	PERMIT SET
3	12/01/2020	PERMIT SET
4	12/01/2020	PERMIT SET
5	12/14/2020	REVISION SET

PROJECT # 2000-0201
DRAWN BY: SLD
CHECK BY: NM
© 2012 Magney Architecture

MISCELLANEOUS
DETAILS

A502

FOR CONSTRUCTION - REVISED 12/14/2020

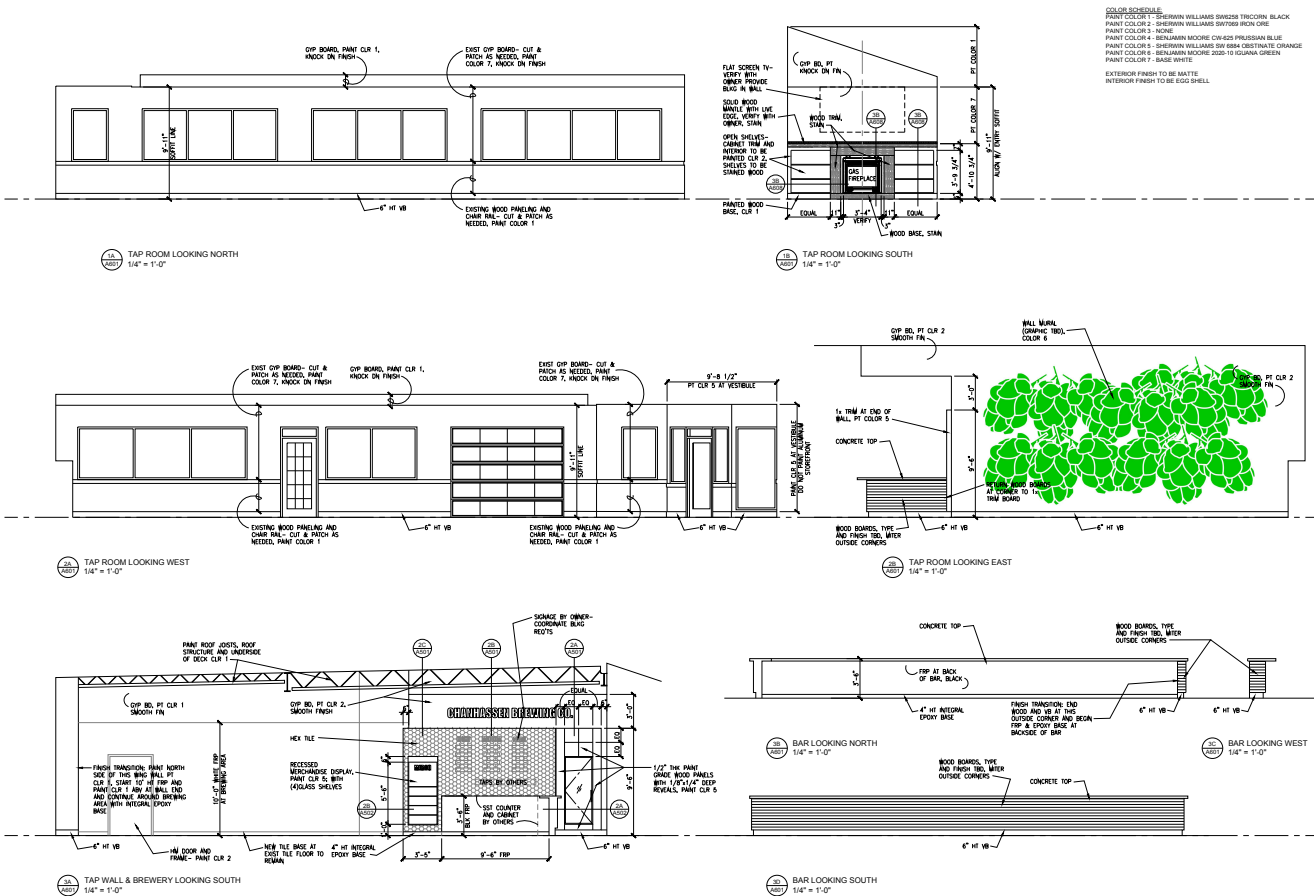

MAGNEY ARCHITECTURE
 + **darin duch**
 4 0 5 1 8 11
 The Commons
 540 Lake Street
 Excelsior, MN 55331
 PH: (612) 701-7117

CHANHASSEN BREWING COMPANY
 951 West 78th Street
 Chanhassen, MN 55317

PROJECT TITLE:
 CHANHASSEN BREWING
 951 West 78th Street
 Chanhassen, MN 55317

SUBMITTAL/REVISIONS:


REVISION	DATE	DESCRIPTION
1	11/14/2019	SCHEMATIC SET
2	11/24/2019	SCHEMATIC SET
3	12/01/2019	PERMIT SET
4	12/01/2019	PERMIT SET
5	12/14/2019	REVISION SET

PROJECT #: 2019-0201
DRAWN BY: MJ
CHECK BY: MJ
 © 2019 Magney Architecture

INTERIOR ELEVATIONS

A601

FOR CONSTRUCTION - REVISED 12/14/2020

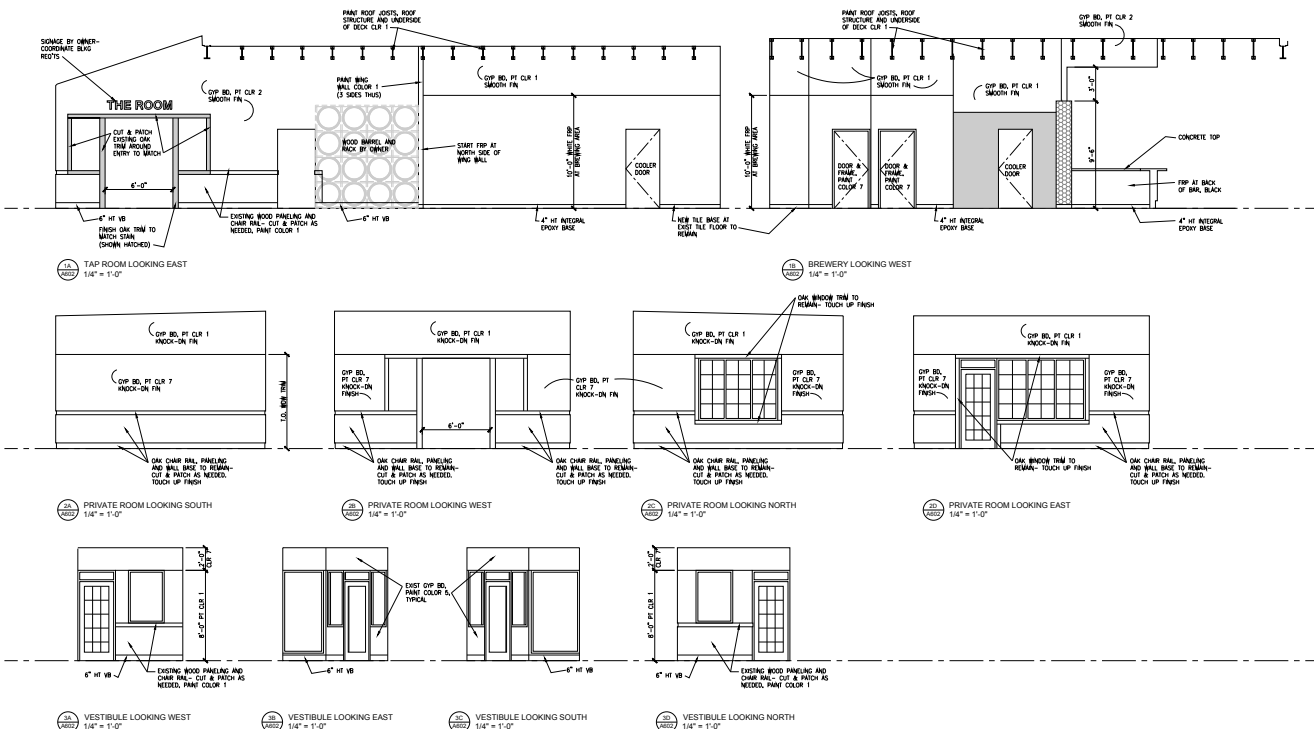

COLOR SCHEDULE
 PAINT COLOR 1 - SHERWIN WILLIAMS SW628 TRICOIN BLACK
 PAINT COLOR 2 - SHERWIN WILLIAMS SW708 BROWN ONE
 PAINT COLOR 3 - NONE
 PAINT COLOR 4 - BENJAMIN MOORE CH-628 PRUSSIAN BLUE
 PAINT COLOR 5 - SHERWIN WILLIAMS SW 684 CRISTALINE ORANGE
 PAINT COLOR 6 - BENJAMIN MOORE 2020-10 KUMAR GREEN
 PAINT COLOR 7 - BASE WHITE
 EXTERIOR FINISH TO BE MATTE
 INTERIOR FINISH TO BE EGGS SHELL

MAGNEY ARCHITECTURE
 + **darin duch**
 The Commons
 540 Lake Street
 Excelsior, MN 55331
 PH: (612) 701-7117

EST. 2019
CHANHASSEN
 BREWING COMPANY

1. HENRY CROSBY HAS THE RIGHT OF FIRST REFUSAL TO PURCHASE THE PROJECT OR ANY PART OF THE PROJECT. IF HENRY CROSBY DOES NOT EXERCISE THIS RIGHT, THE PROJECT WILL BE OFFERED TO THE OTHER PARTY. THIS AGREEMENT IS SUBJECT TO THE TERMS AND CONDITIONS OF THE SALE OF THE PROJECT.

James S. Magney
 Tommy S. Magney
 LICENSE NUMBER: 19917
 JUNE 30, 2022

PROJECT TITLE:
 CHANHASSEN BREWING
 951 West 78th Street
 Chanhassen, MN 55317

SUBMITTAL/REVISIONS:


REVISION	DATE	DESCRIPTION
1	11/04/2020	SCHEMATIC SET
2	11/04/2020	PERMIT SET
3	12/01/2020	PERMIT SET
4	12/01/2020	PERMIT SET
5	12/14/2020	REVISION SET

PROJECT #: 2020-0201
DRAWN BY: MJ
CHECK BY: MJ
 © 2022 Magney Architecture

INTERIOR ELEVATIONS

A601

FOR CONSTRUCTION - REVISED 12/14/2020

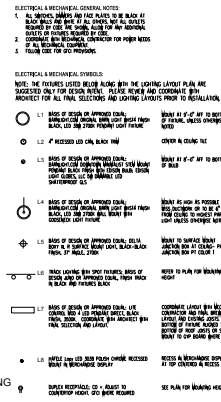

MAGNEY ARCHITECTURE		
+ darin duch design		
The Commons 540 Lake Street Suamico, MN 55331 PH: (612) 701-7117		
		
CHANHASSEN BREWING COMPANY		
A HENRI CHERRY CRAFT BEER TAPROOM LOCATED IN THE CHANHASSEN BREWERY PREPARED BY ME OR UNDER MY DIRECT SUPERVISION AND SEAL I AM A DULY LICENSED ARCHITECT USING THE SEALS OF THE STATE OF MINNESOTA		
<i>Darín Duch</i>		
Darín S. Magney LICENSE NUMBER: 10677 JUNE 30, 2022		
PROJECT TITLE:		
CHANHASSEN BREWING		
951 West 78th Street Chanhasen, MN 55317		
SUBMITTAL REVISIONS		
MARK	DATE	DESCRIPTION
(1)	11/16/2020	DRINK PUMP SET
(2)	11/24/2020	PUMP SET
(3)	02/09/2020	PUMP SET
(4)	12/14/2020	REVISION SET
PROJECT # _____ 2020-020		
DRAWN BY _____		
CHECK BY _____		
© 2019 Magney Architecture Inc.		
PROPOSED REFLECTED CEILING PLAN		
A701		